



Instalación Fotovoltaica Resumen Técnico

DATOS DEL CLIENTE

Nombre: **Alejandro Fiermarin**

Dirección: **Sigrist y Fender 1291**

Ciudad: **Nueva Helvecia, Colonia**

Celular: **099 550 725**

Fecha prevista: **4ta semana abril**

DATOS SITIO DE INSTALACIÓN

**Tipo
techo**

- ☐ Isopanel
☐ Hormigón
☒ Chapa
☐ Tejas
☐ Otro:

Info techo:

Techo de chapa sobre tubular de hierro, orientación norte, fijada con tornillos punta mecha. Tamaño 7,5 x 4,3 mts.

- 6 paneles inclinados 25° atrás
- 4 paneles al ras del techo adelante

DATOS ELÉCTRICOS

Cantidad Paneles: **10**

Potencia Paneles: **580W**

Inversor: **Growatt de 6kW**

Strings/Líneas DC: **2**

Cable AC: **Superplastico 2x6mm²**

Térmica AC: **32 A**

Diferencial AC: **40 A, 300mA**

Largo cables AC (aprox): **5 mts**


Largo cables DC (aprox): **20 mts**


OTROS DATOS


Altura techo: **2 pisos**


Red:

- ☒ Monofásica
☐ Trifásica 230 (sin neutro)
☐ Trifásica 400 (con neutro)

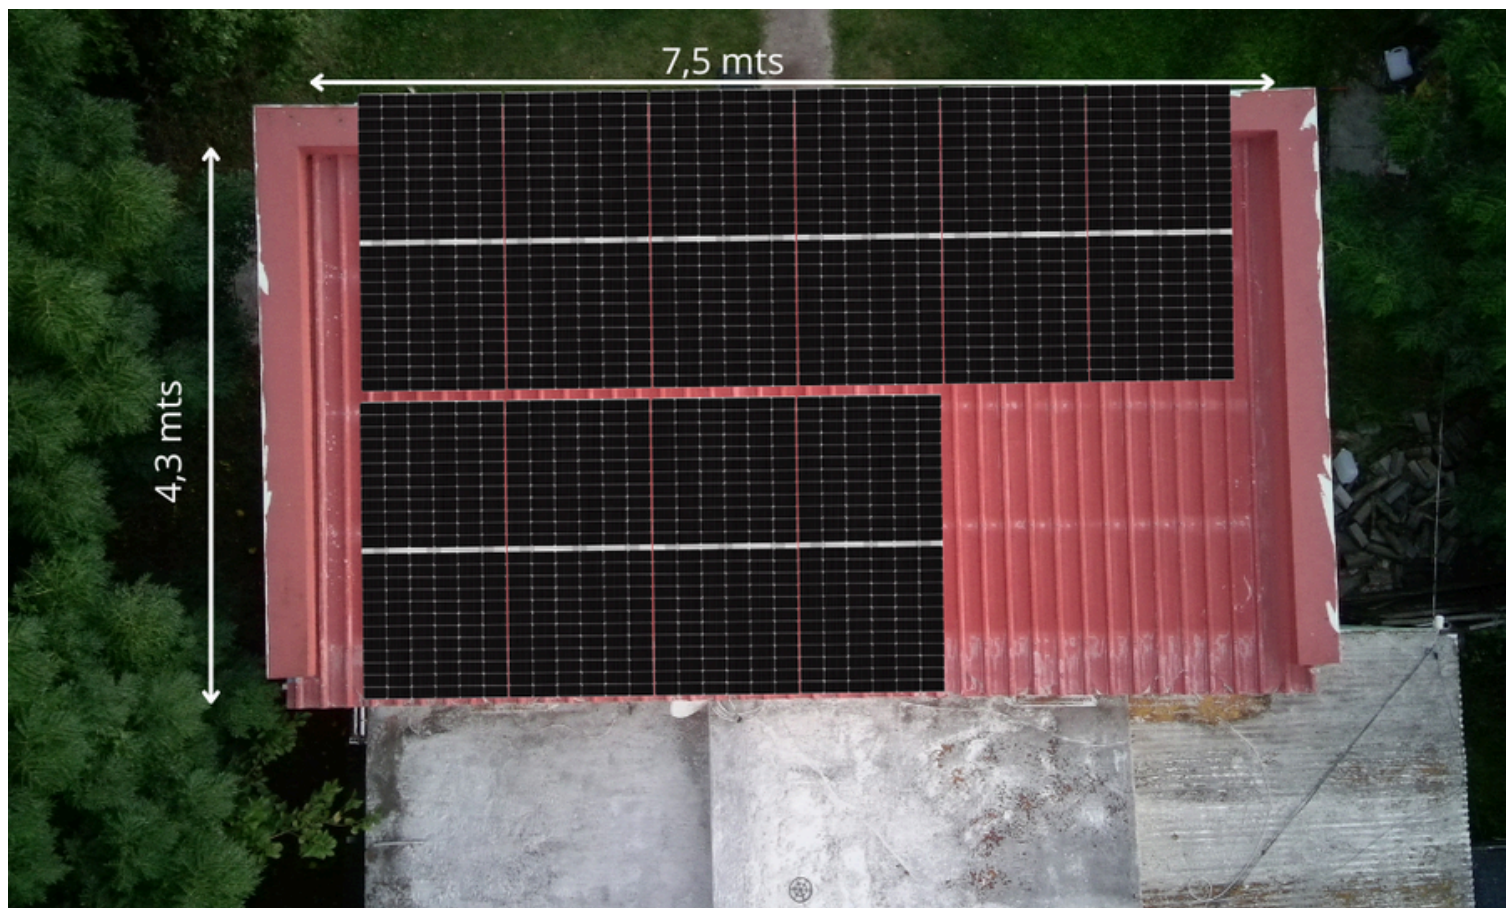

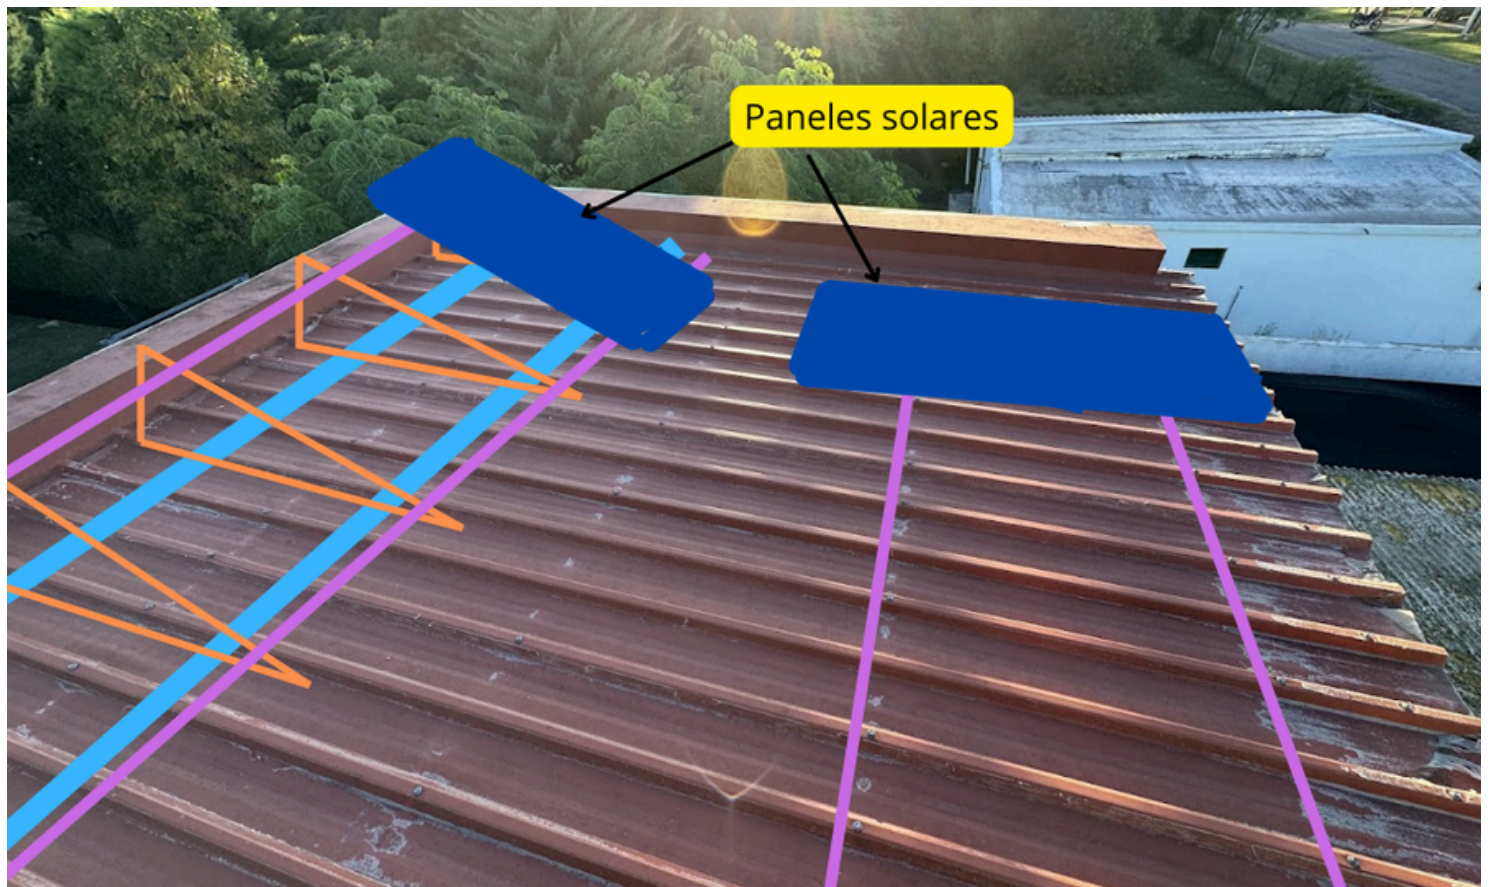

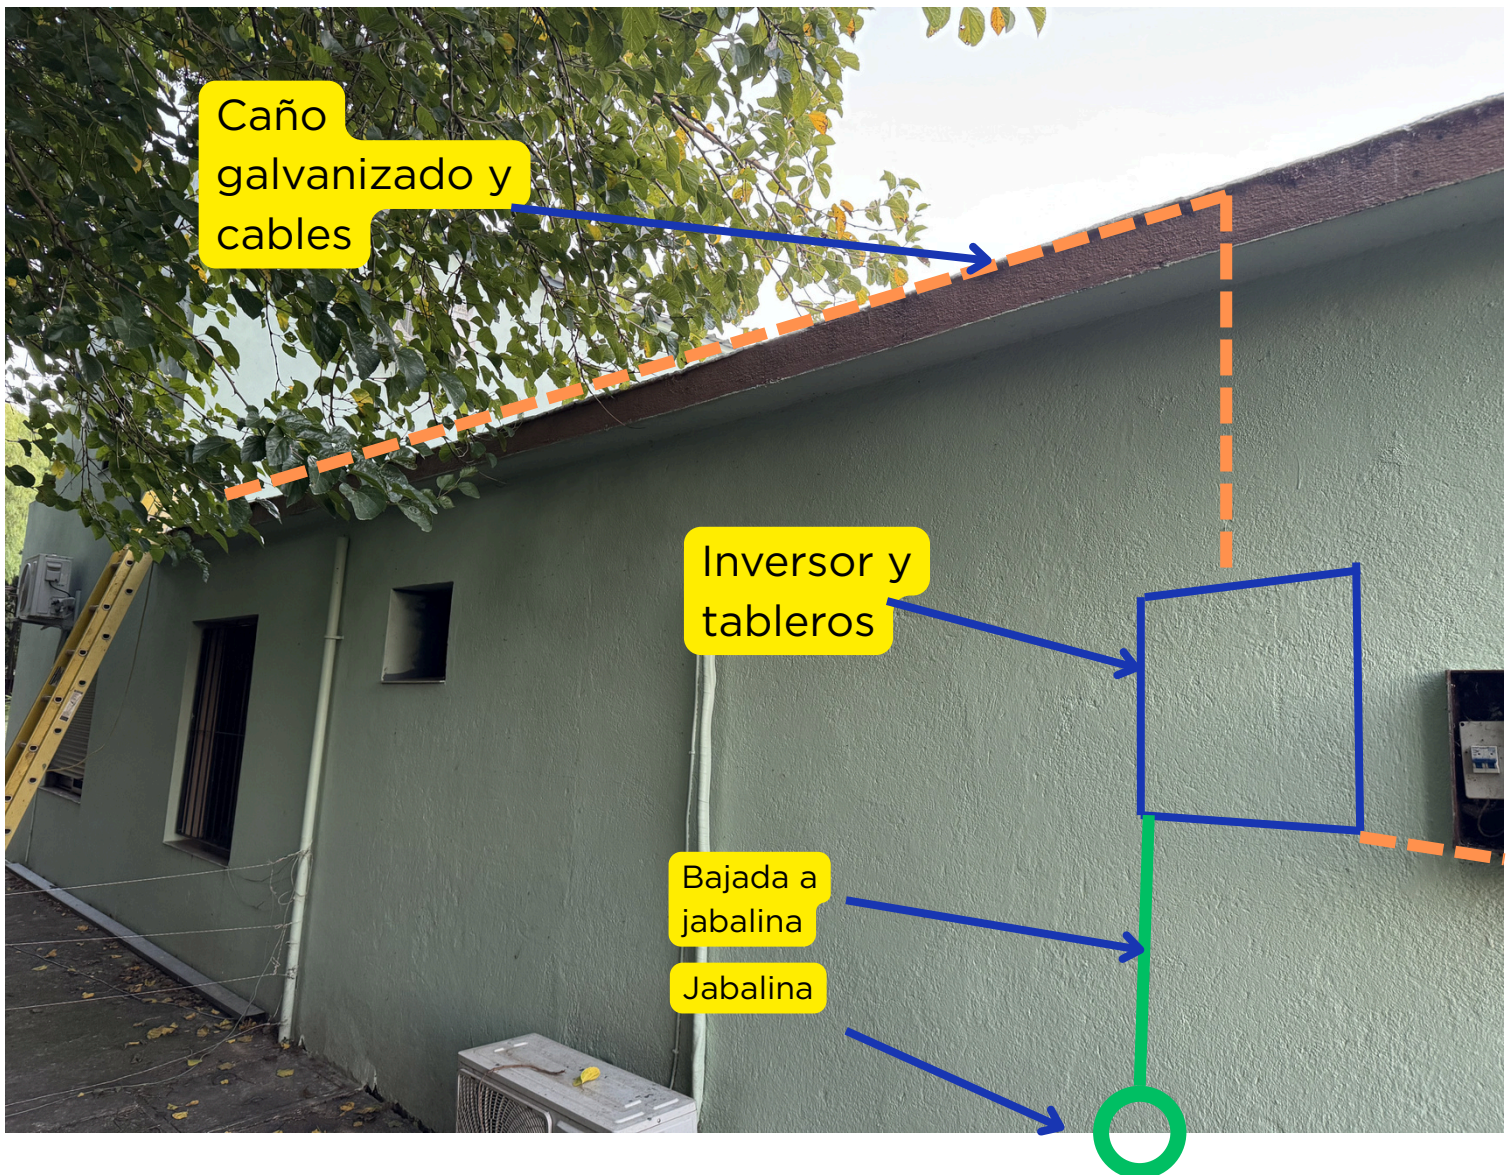

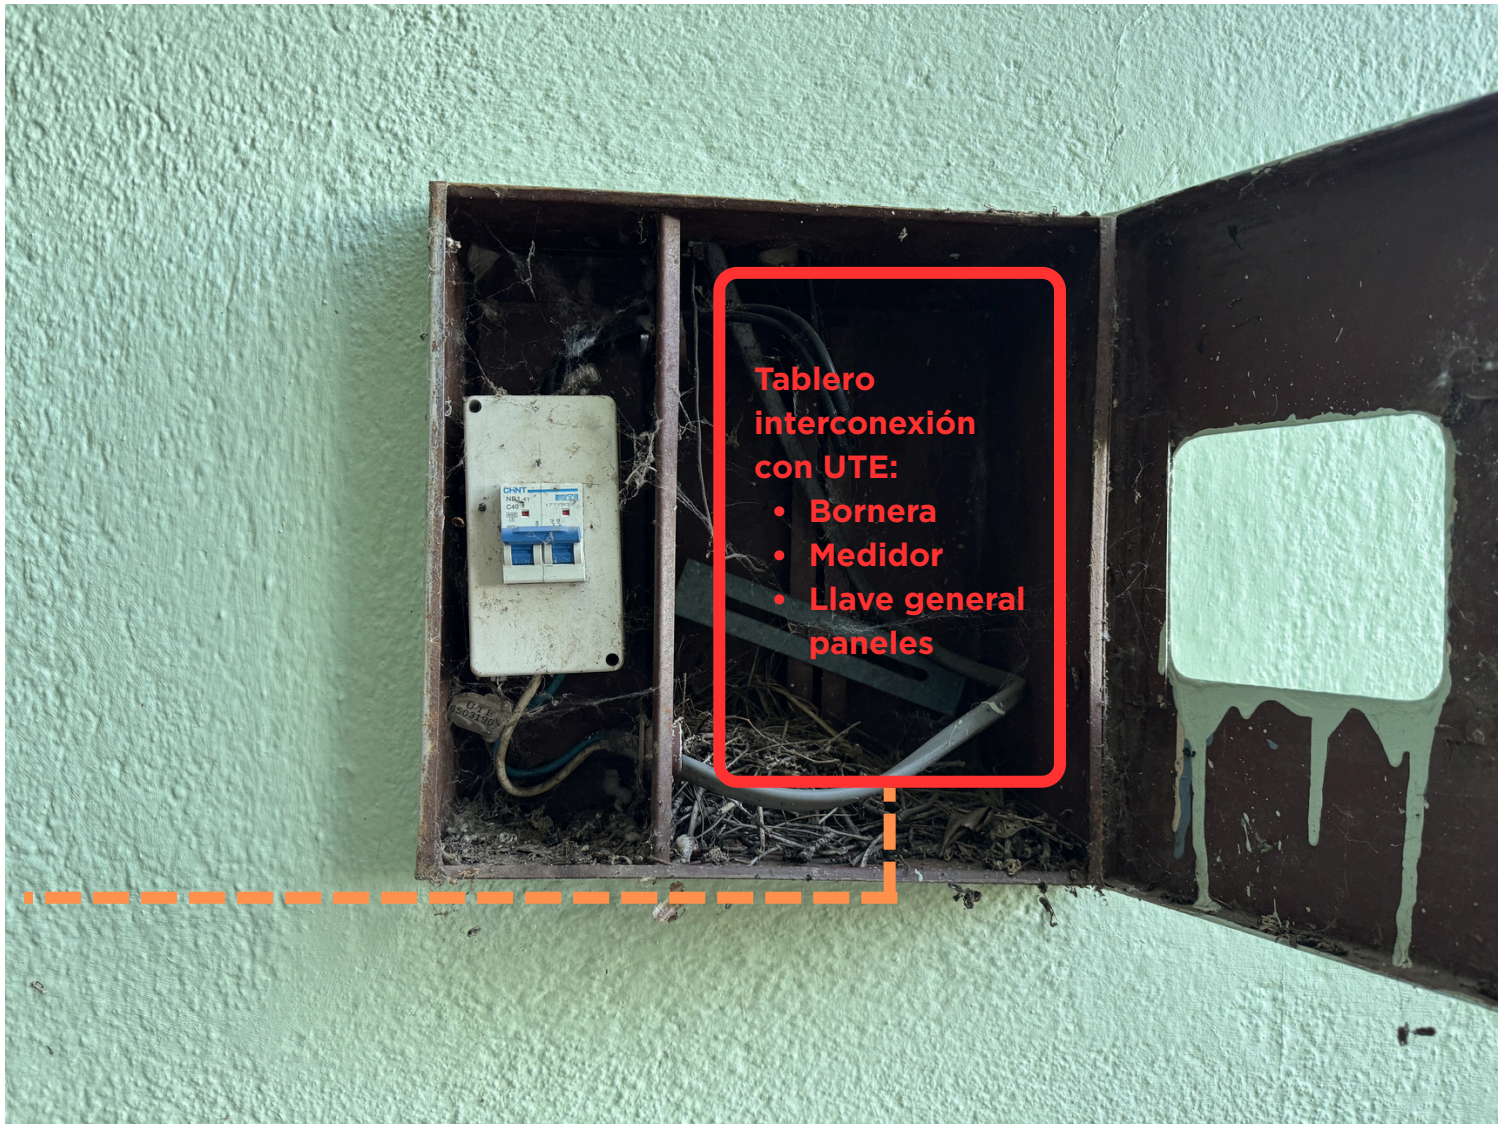

**Tablero
interconexión
con UTE:**

- **Bornera**
- **Medidor**
- **Llave general
paneles**